




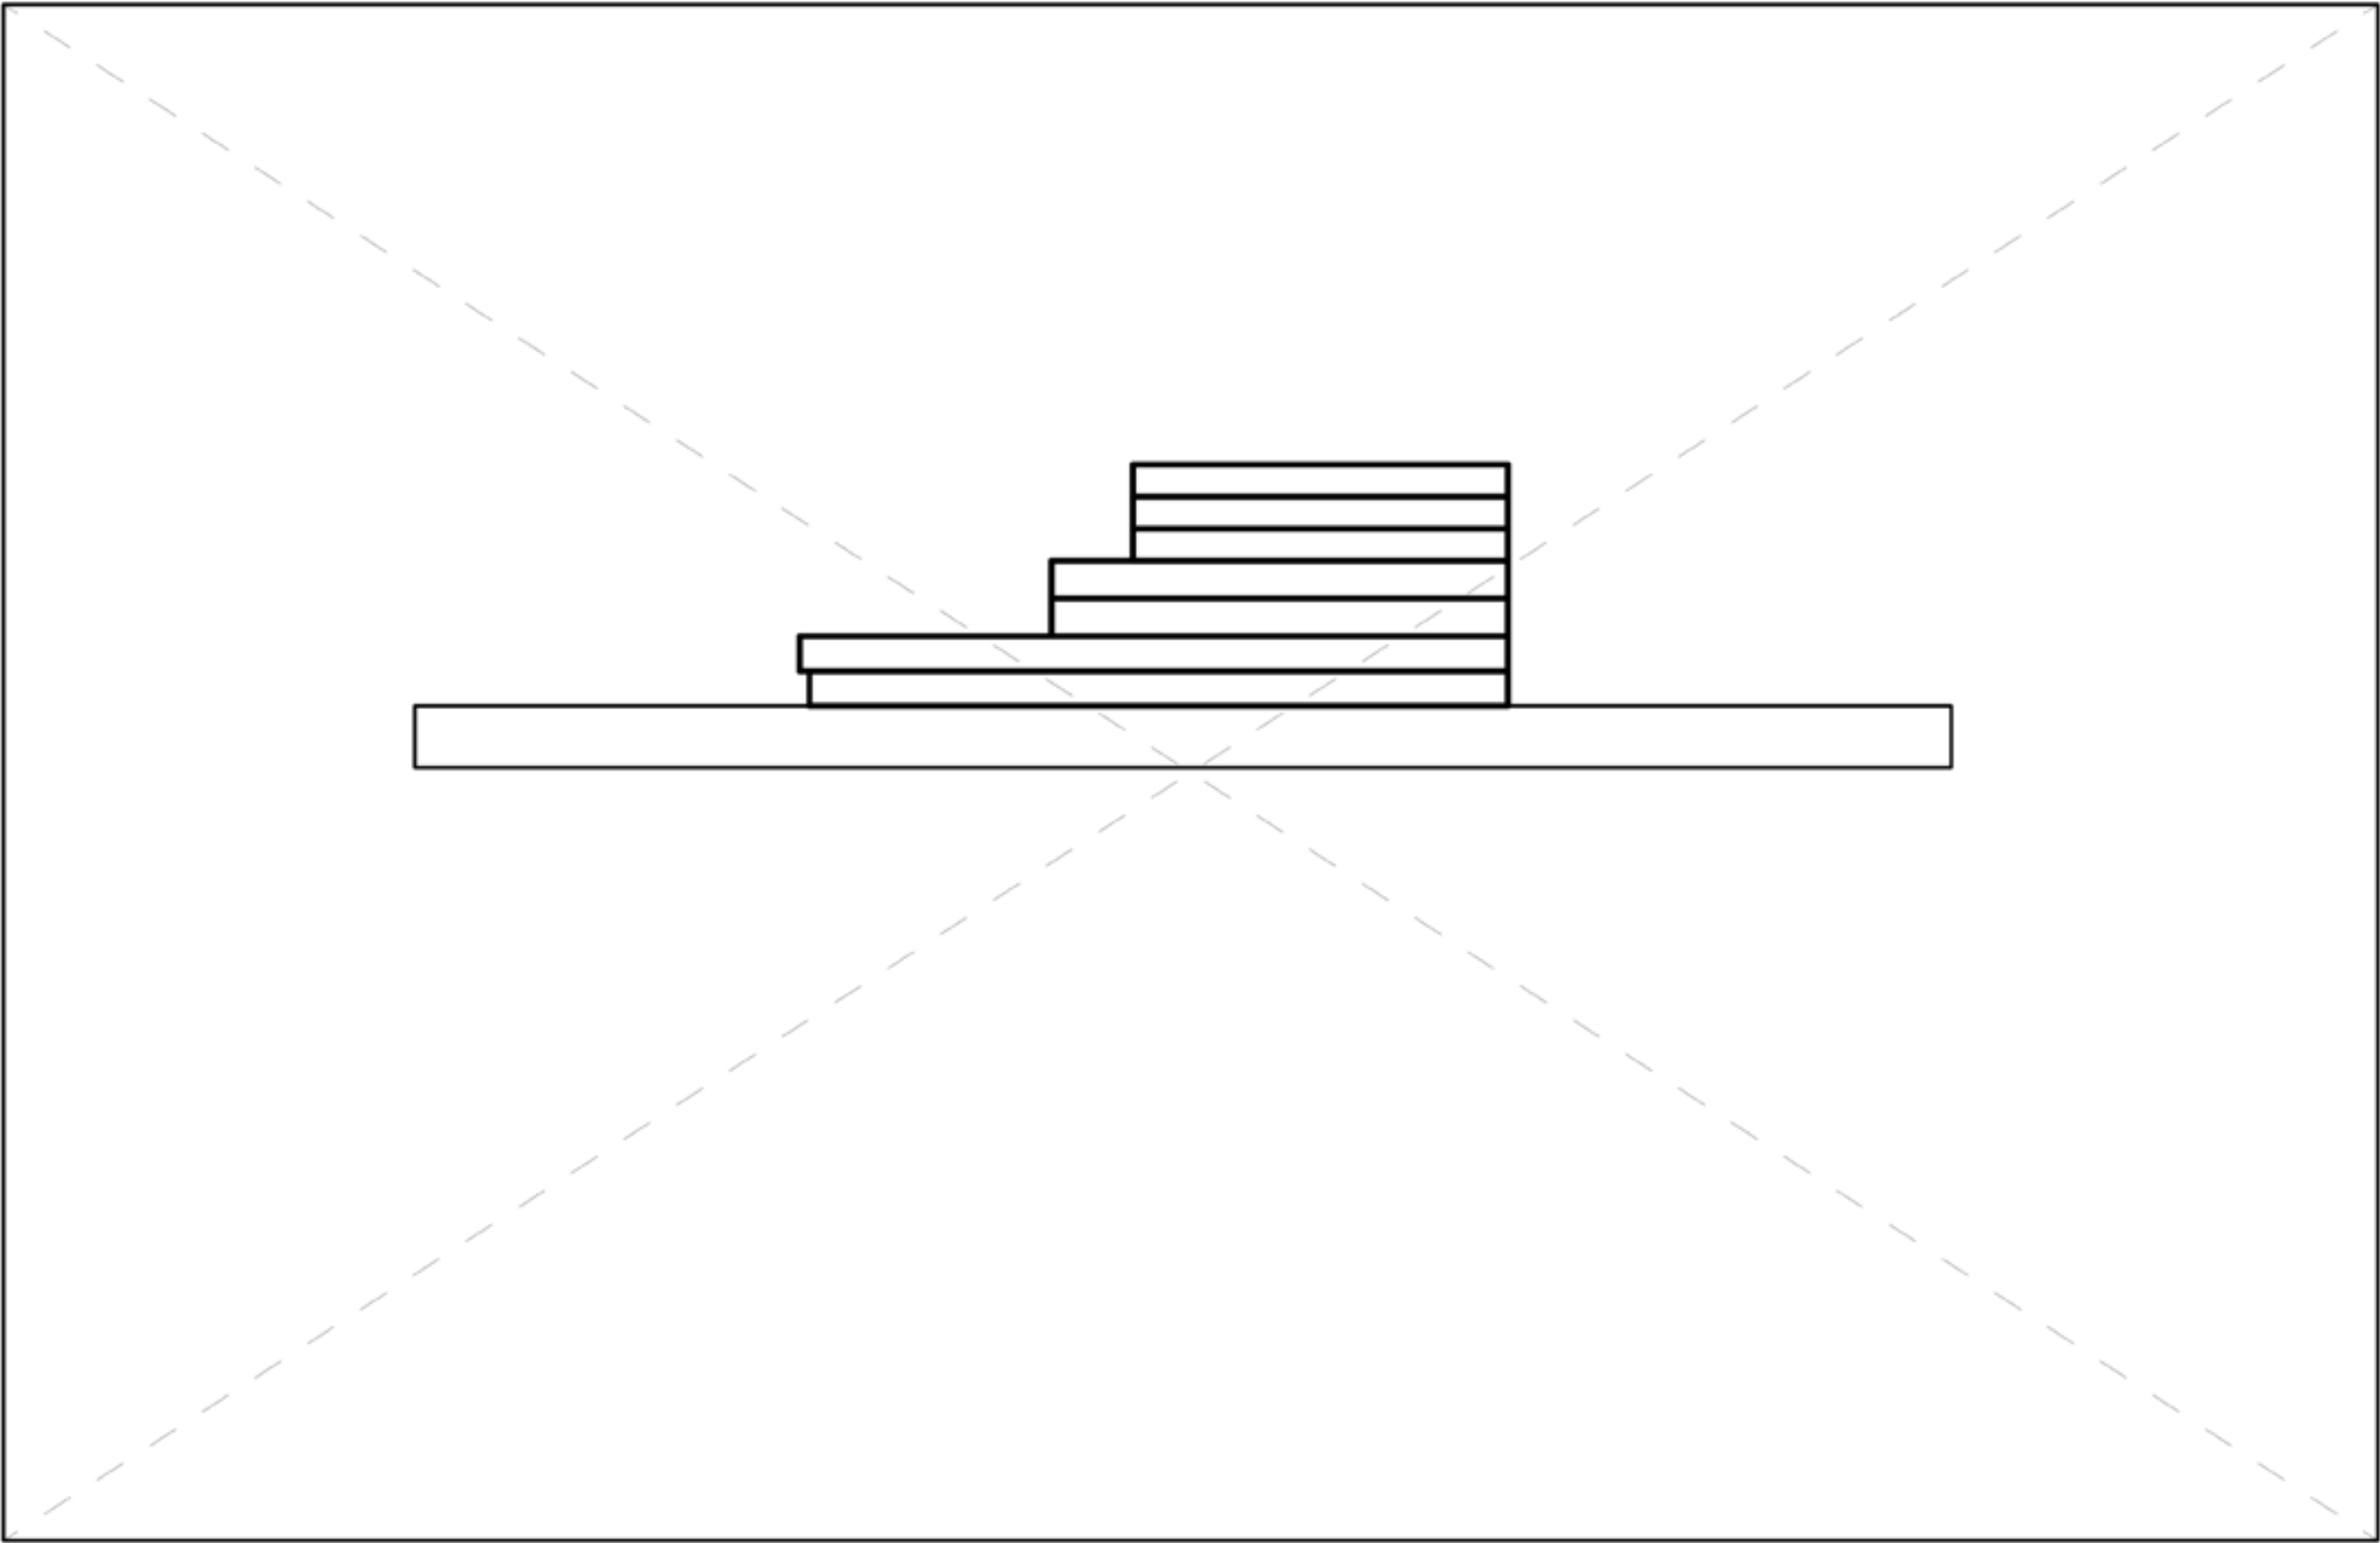


Volume 05
Visualizing Architecture

Alex Hogrefe





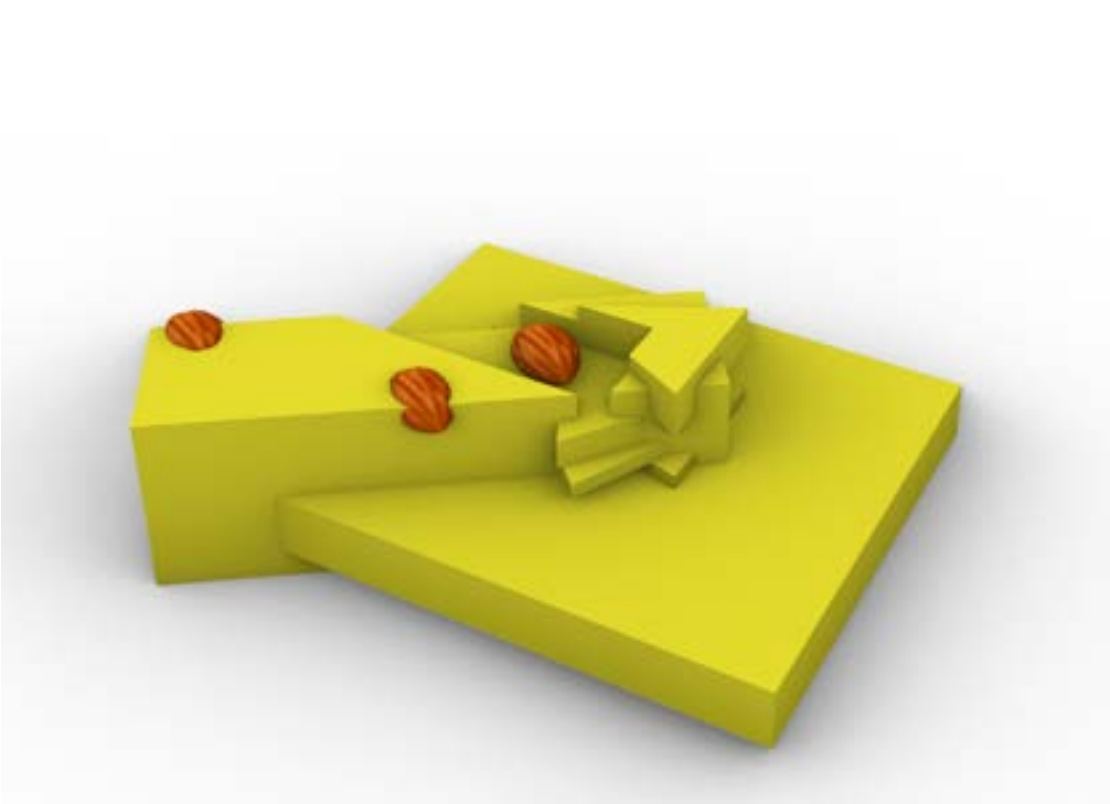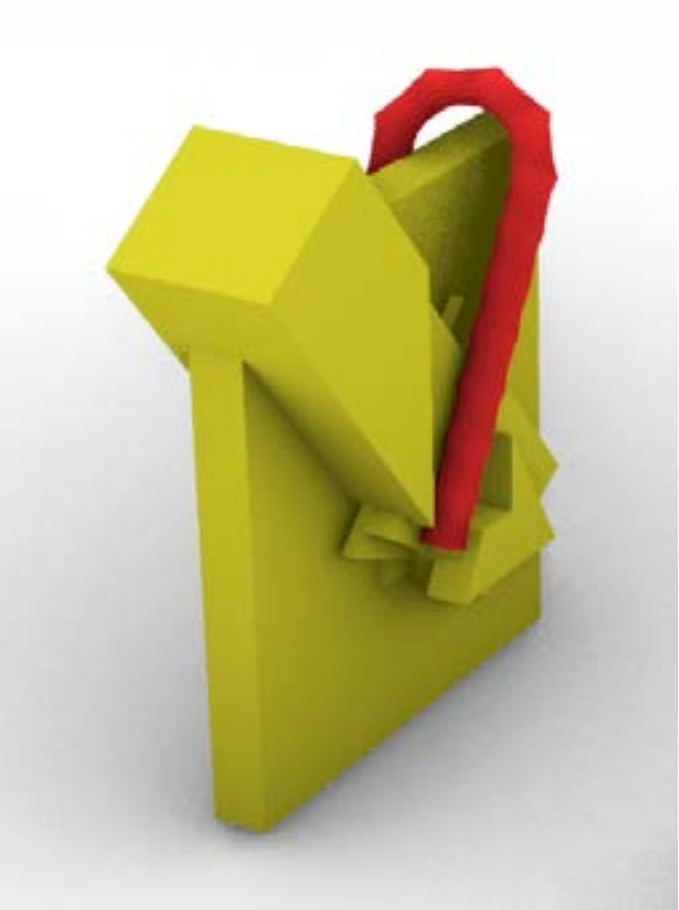
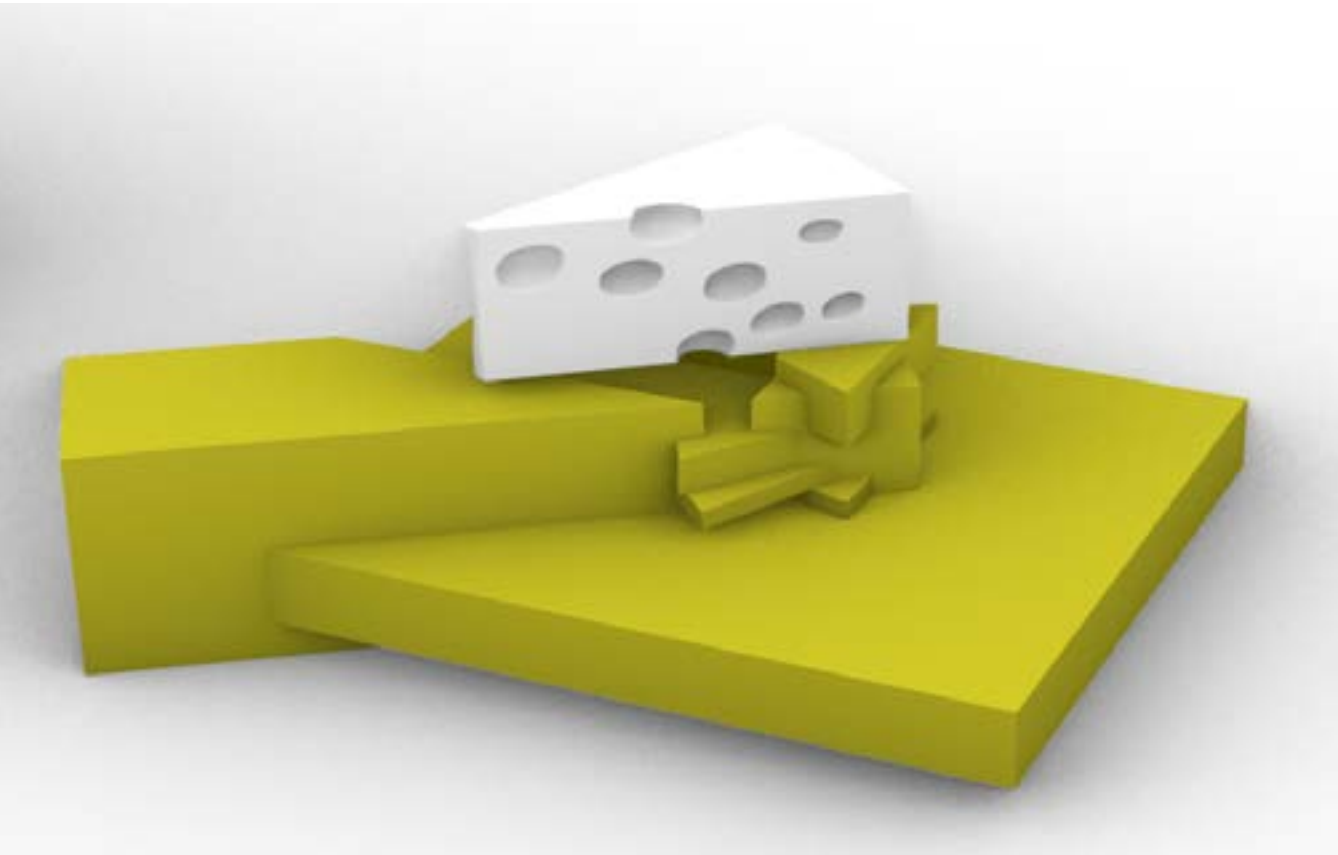





Louis Kahn Architecture
Trenton Bath House, New Jersey, 1955
Adam Miller
Arh 650 25 AAU




- 1. basket room (check-in)
- 2. atrium - open to the sky
- 3. porch (stairs up to pool)
- 4. women's dressing area
- 5. men's dressing area
- 6. baffled entries
- 7. pool manager office
- 8. pool machine office
- 9. storage

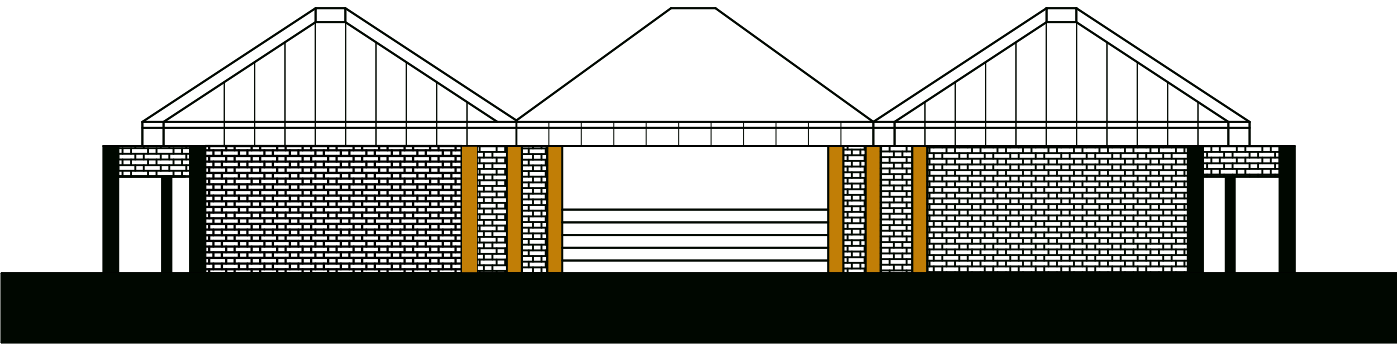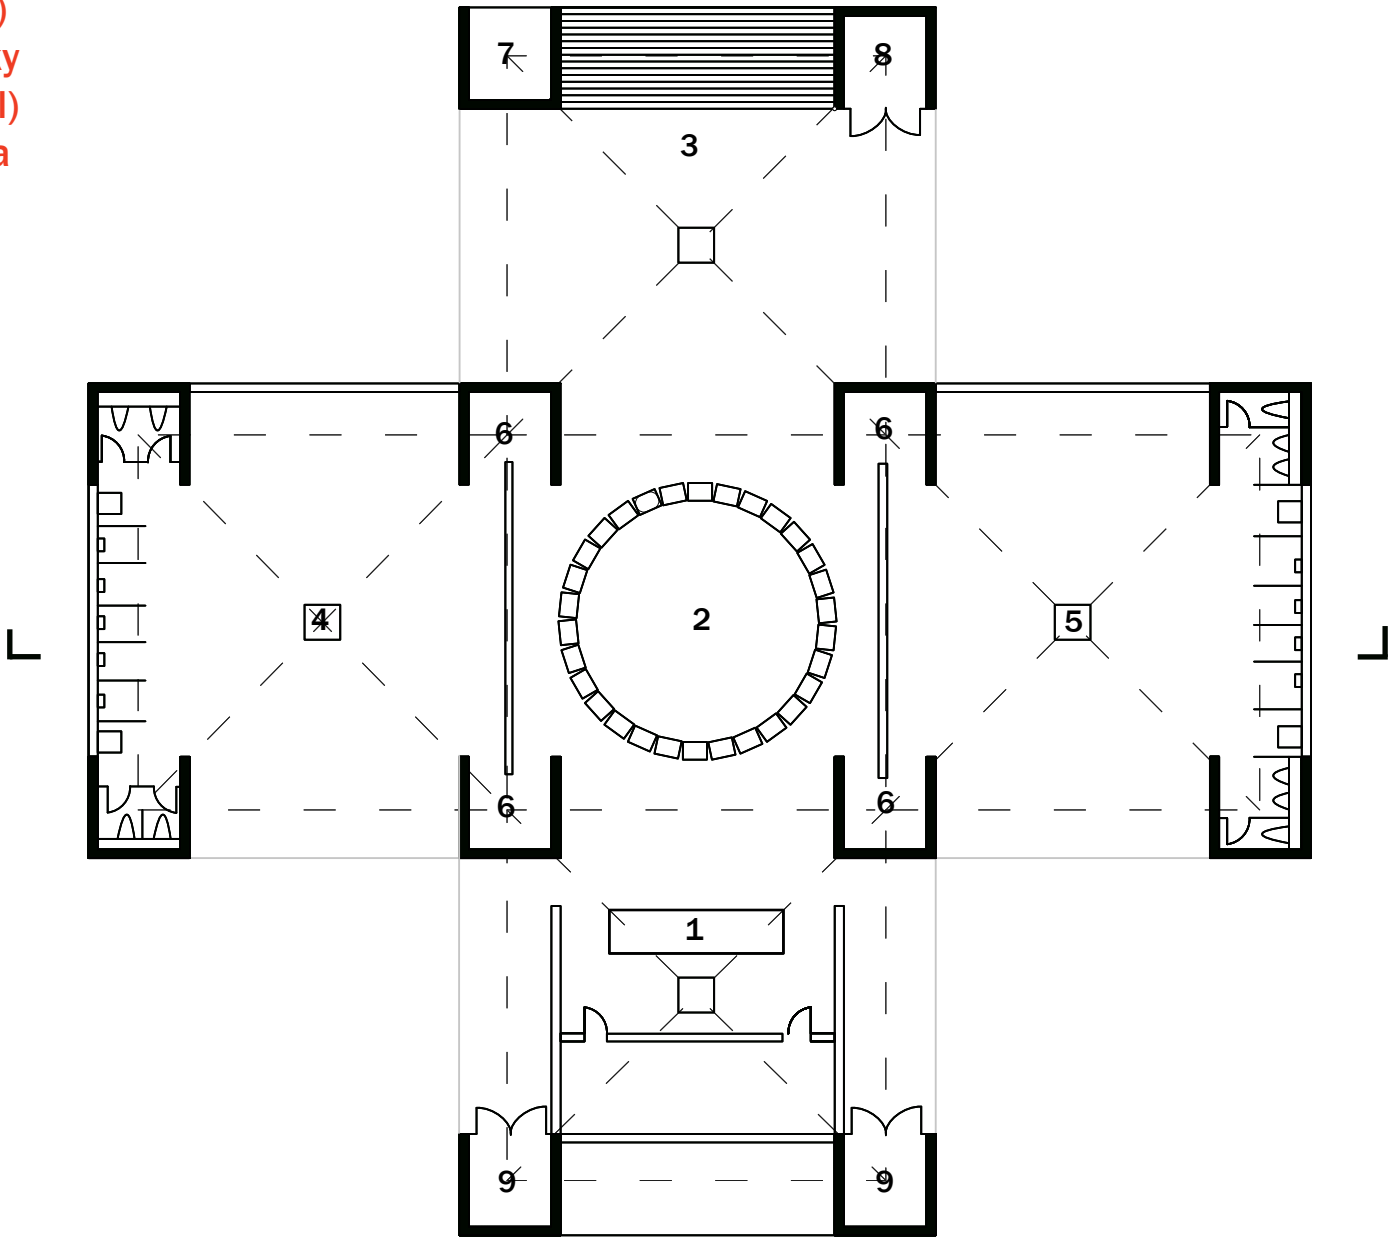


Louis Kahn
Trenton Bath House, New Jersey, 1955
Case Study | Student: Altankhuyag Dash

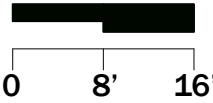

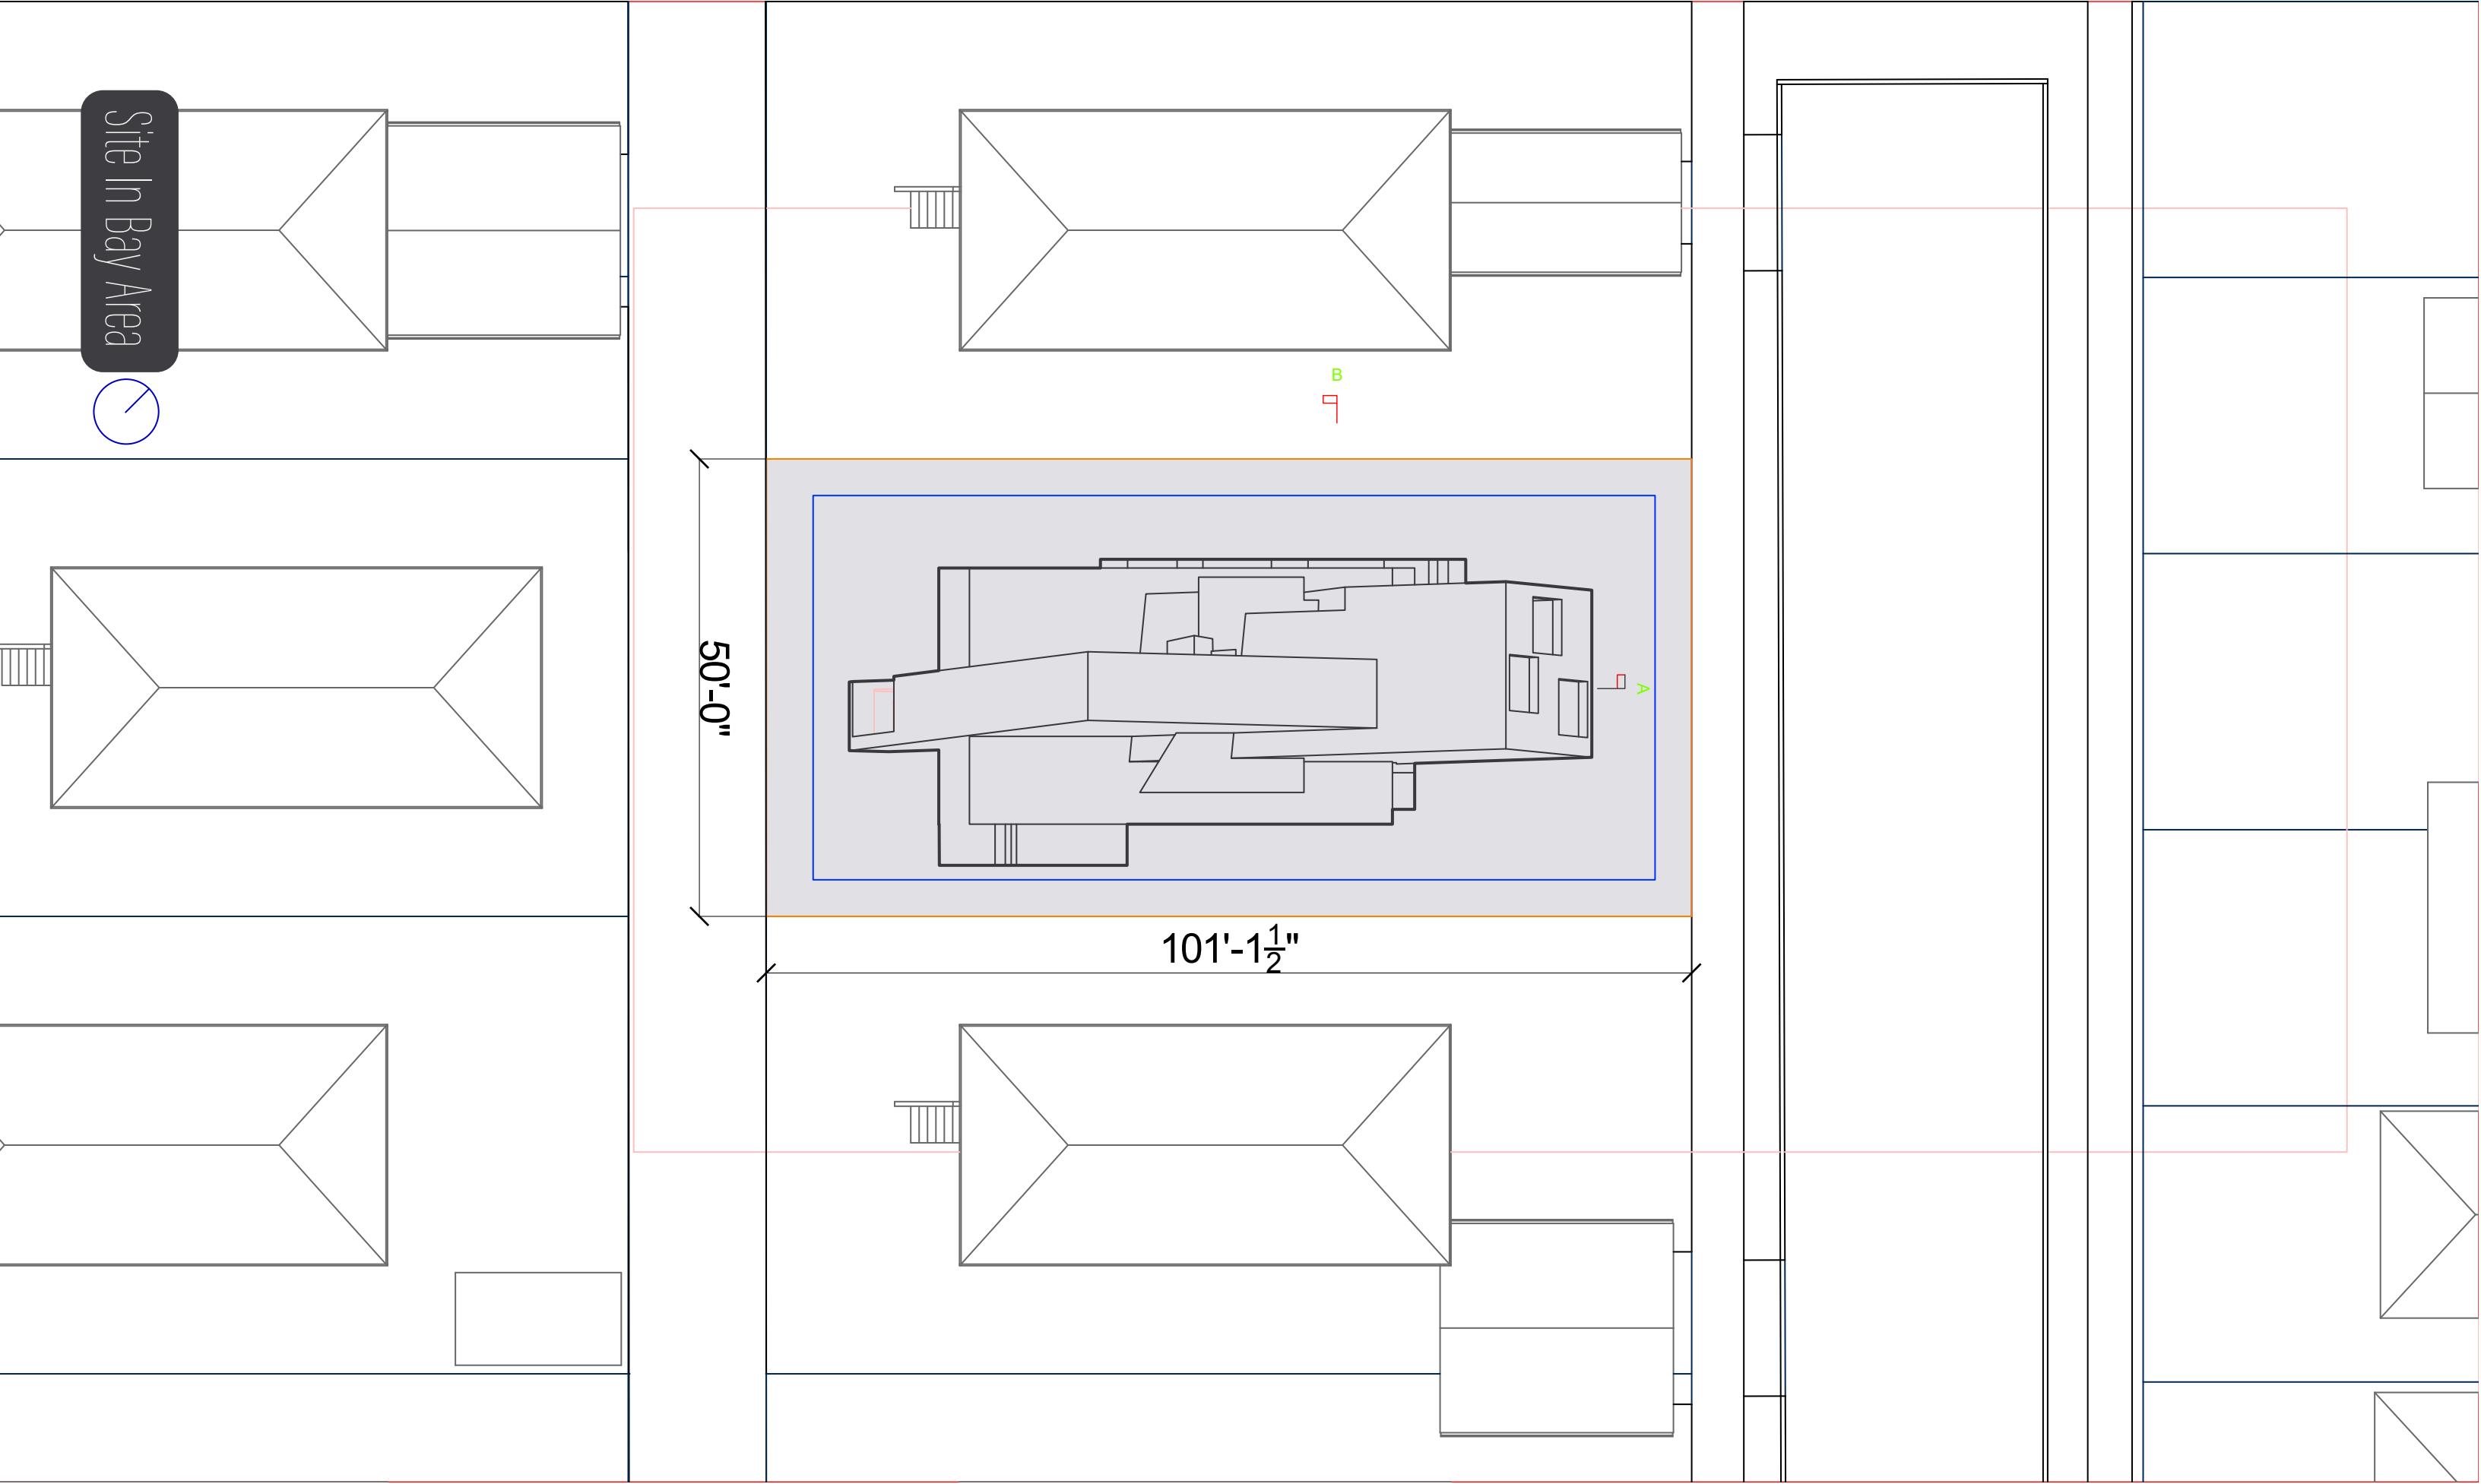


- Program Key
- 1. N/A
 - 2. Toilet
 - 3. Bath
 - 4. Relax
 - 5. Eat
 - 6. N/A
 - 7. Other
 - 8. Floyed

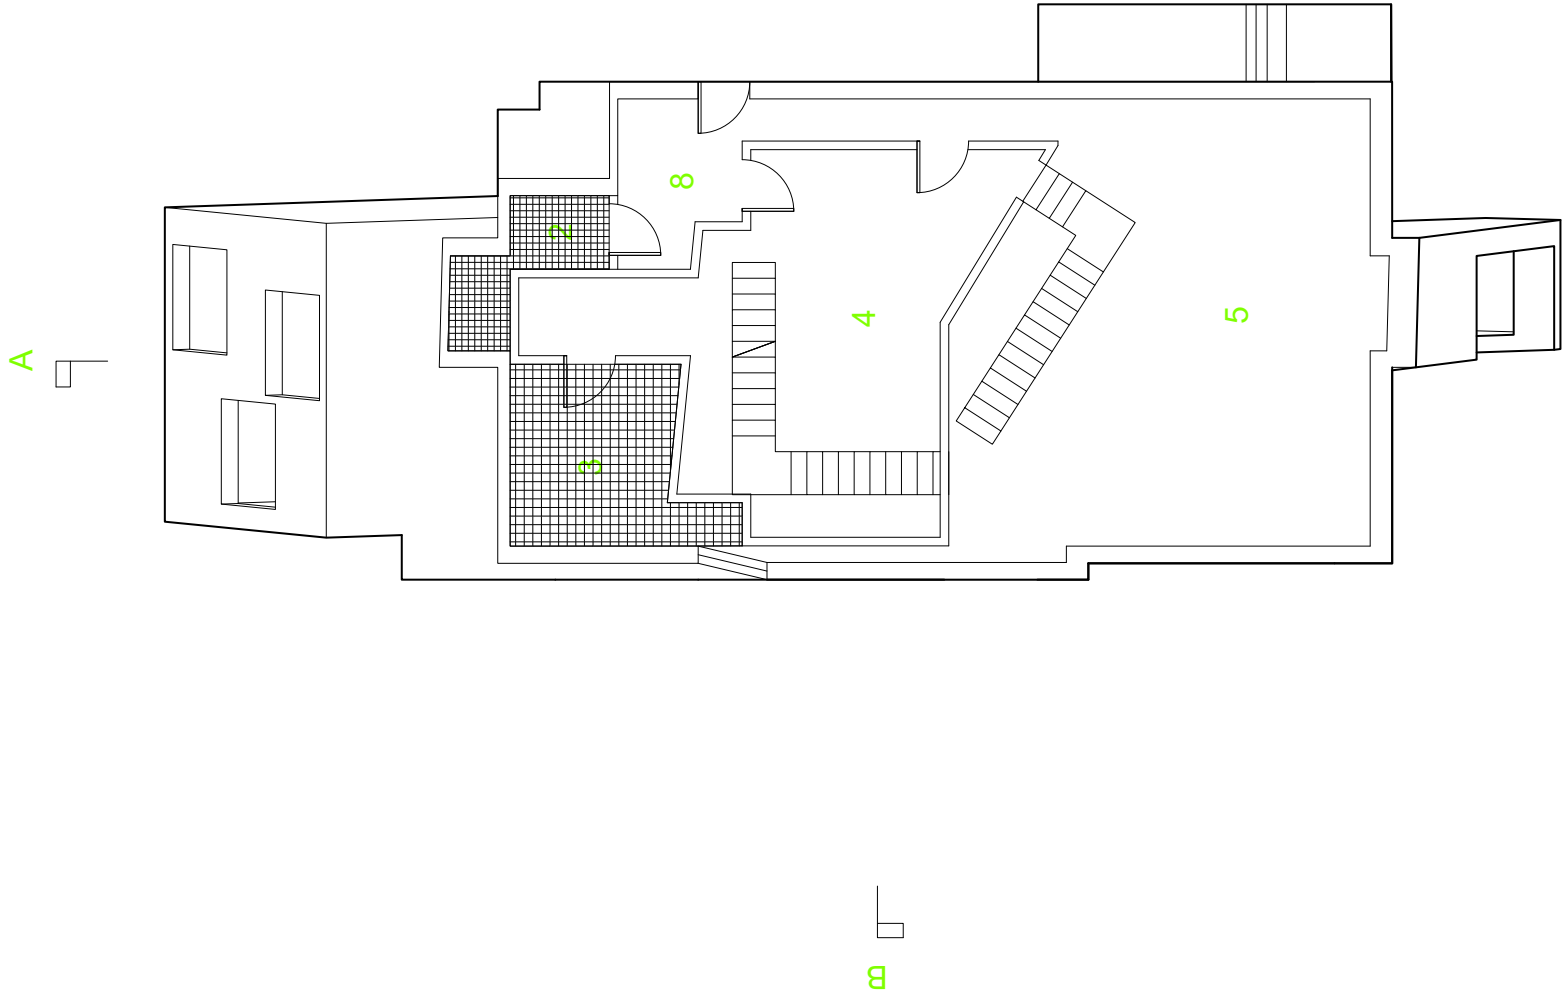

Ground Floor




Program Key
8. Office & study
room
4. Relax

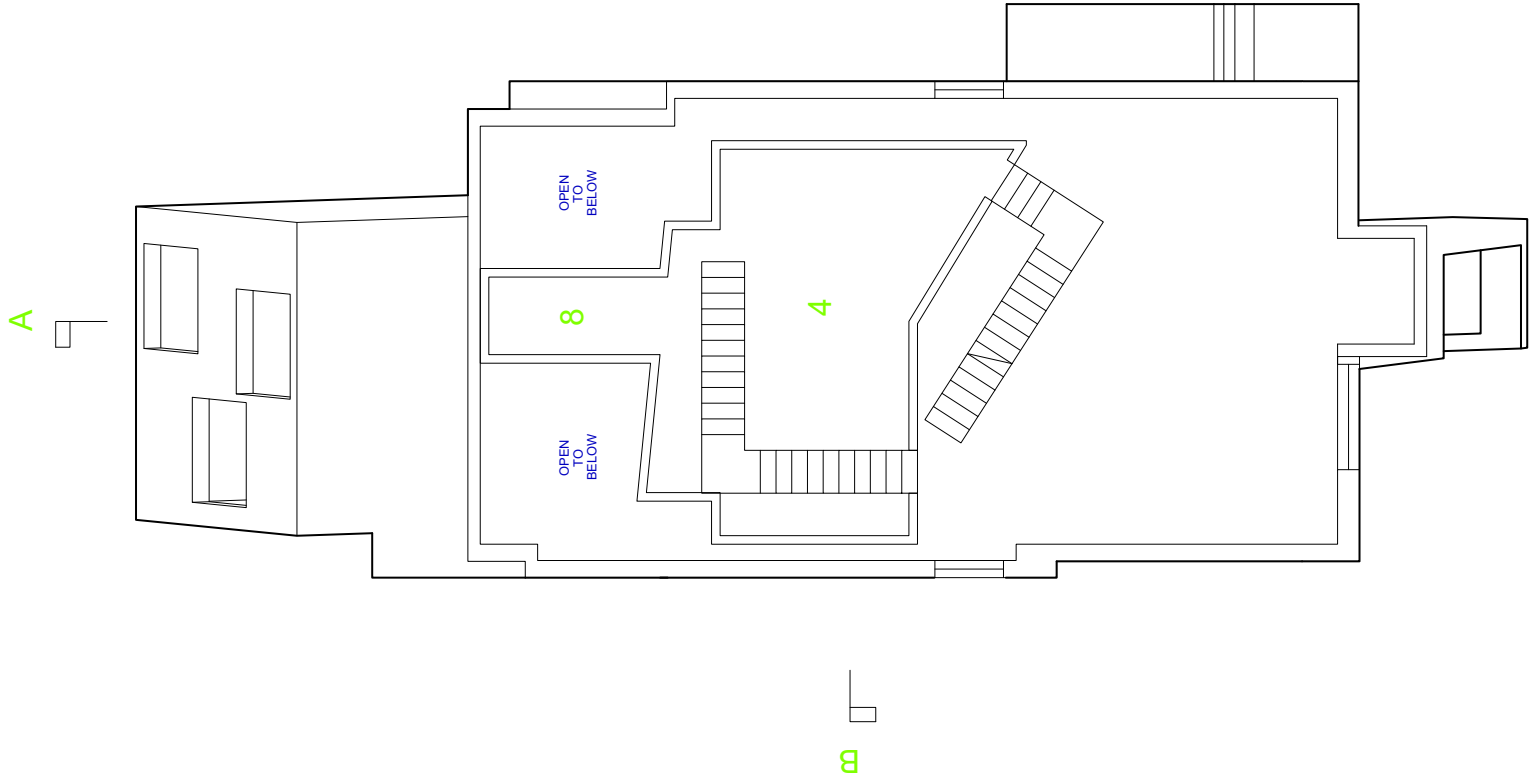


Plan Level 2




Program Key
8. Office & study
room
4. Relax

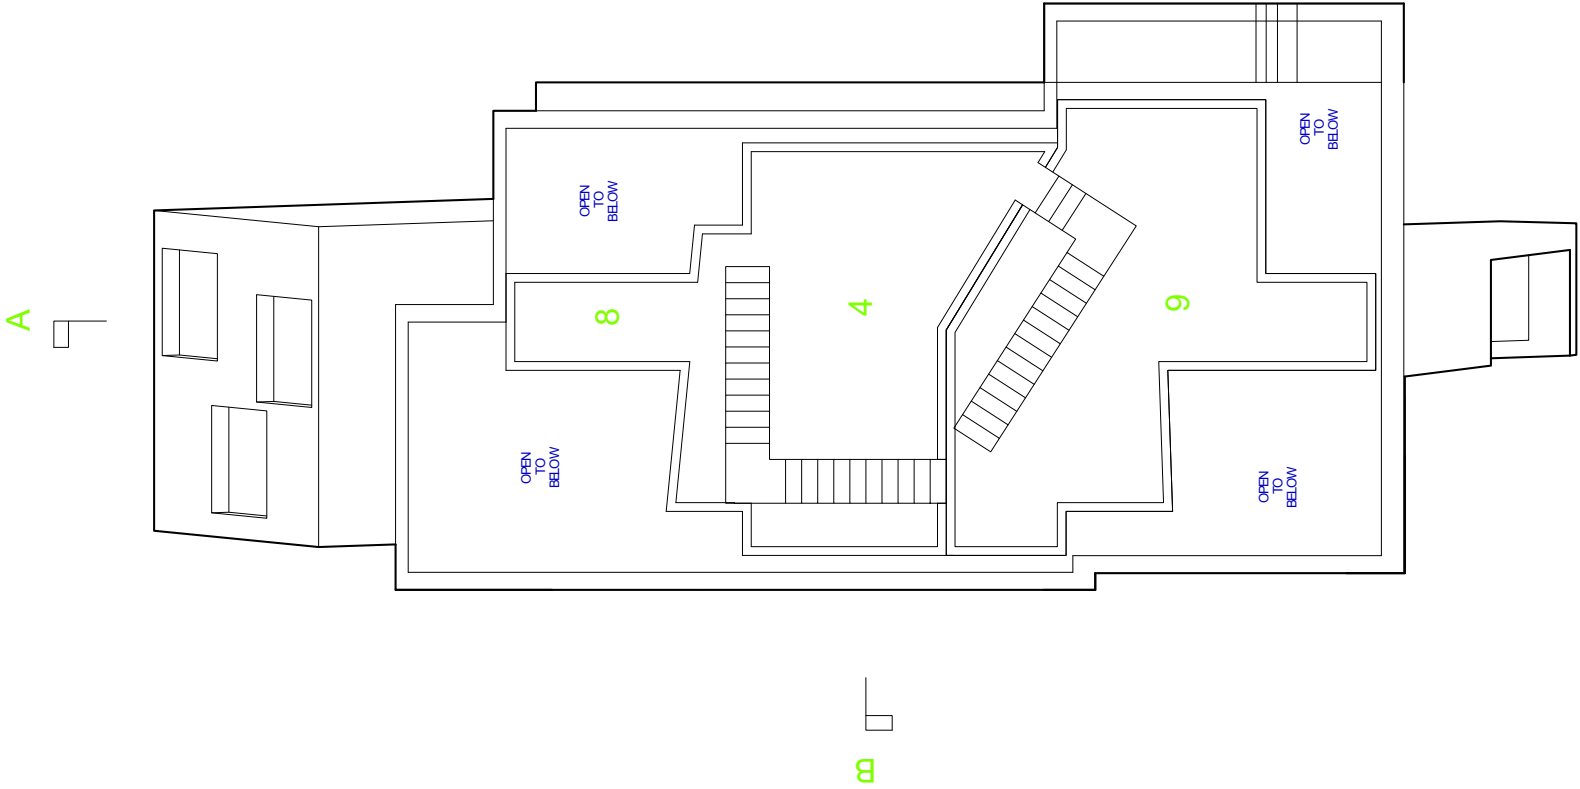

Plan Level 3

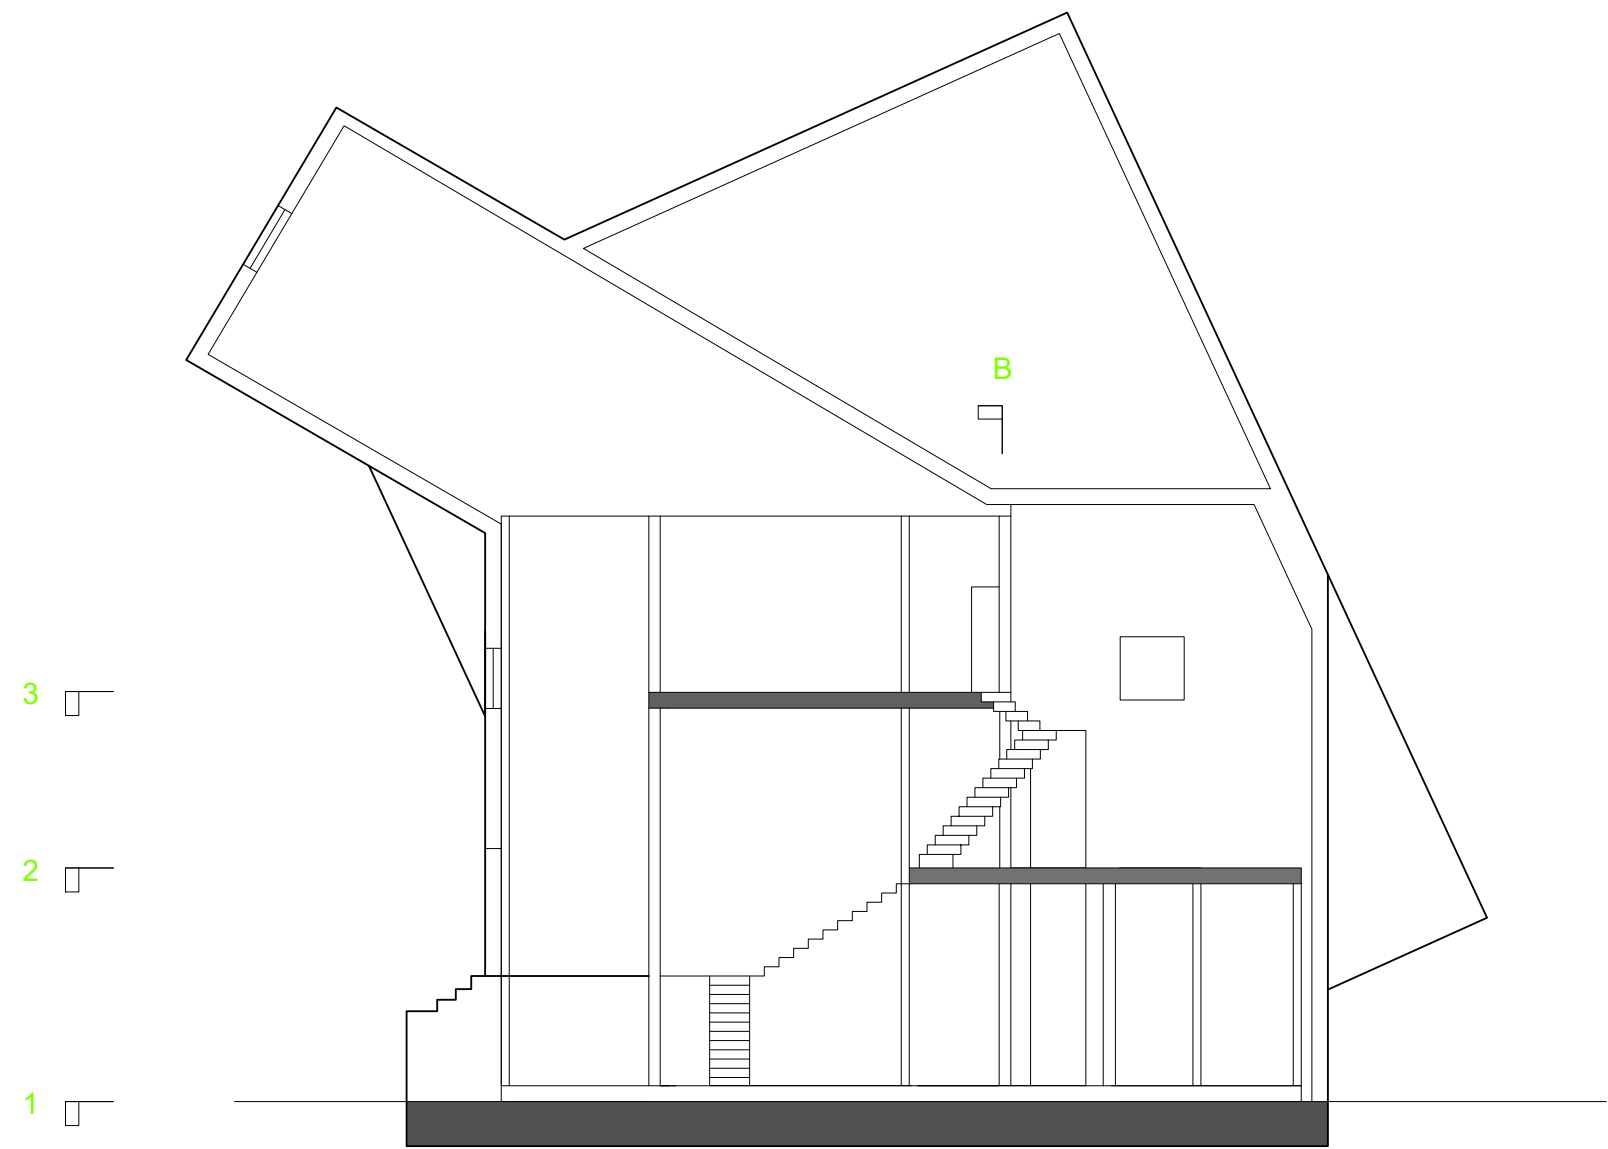

House for Triangle Toy
Section A, 1/8"=1'

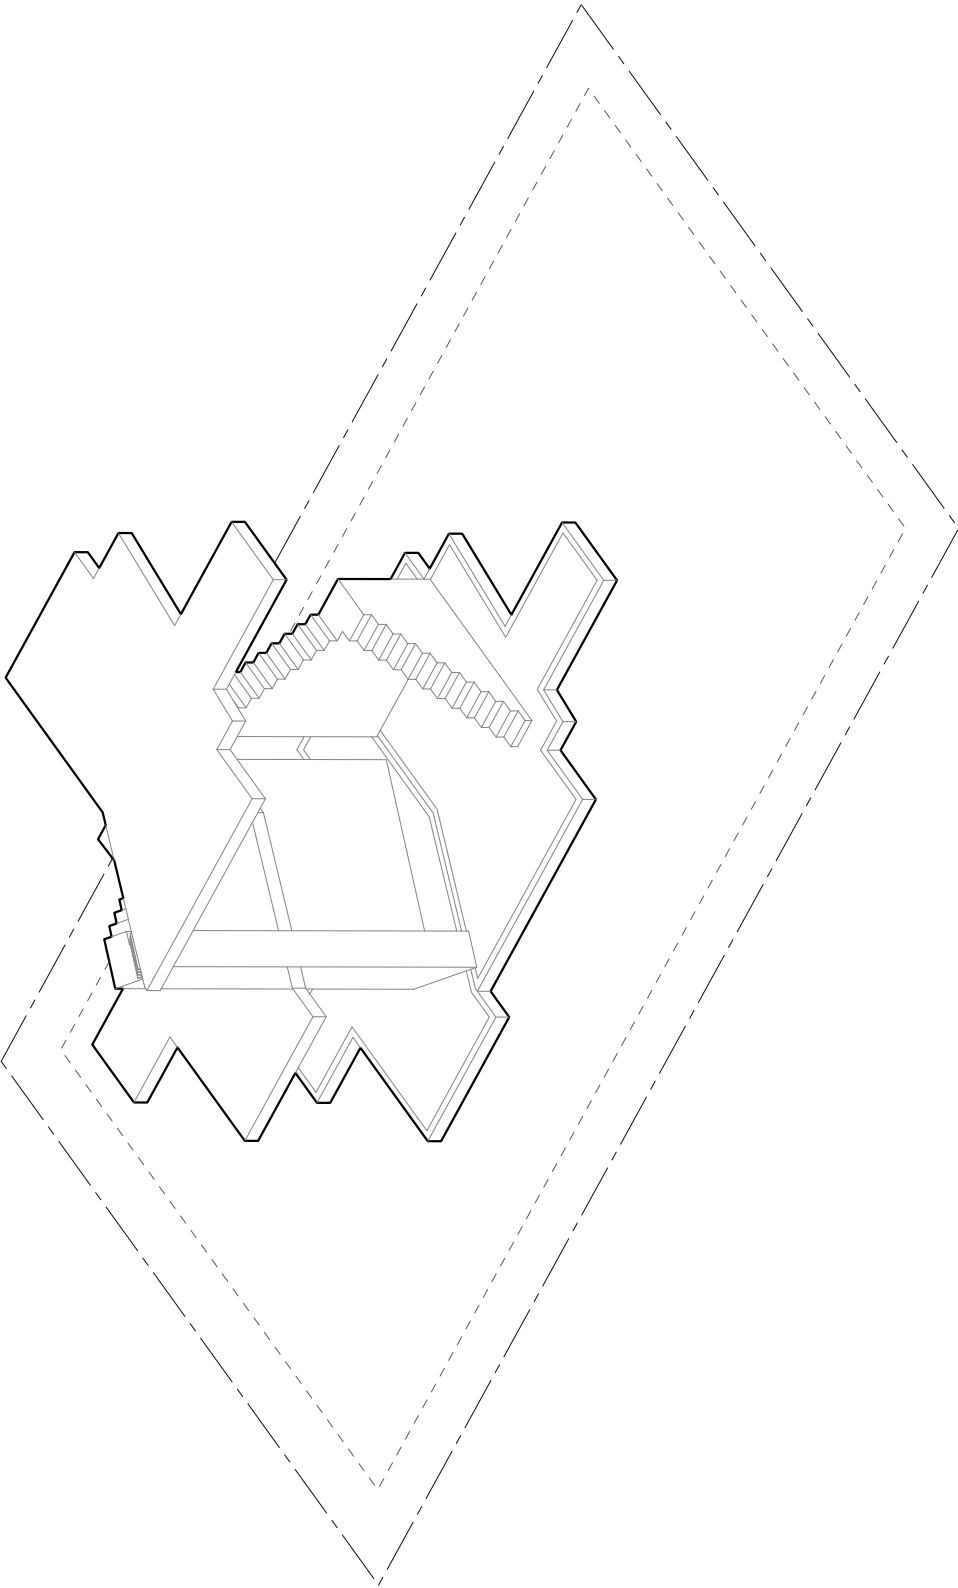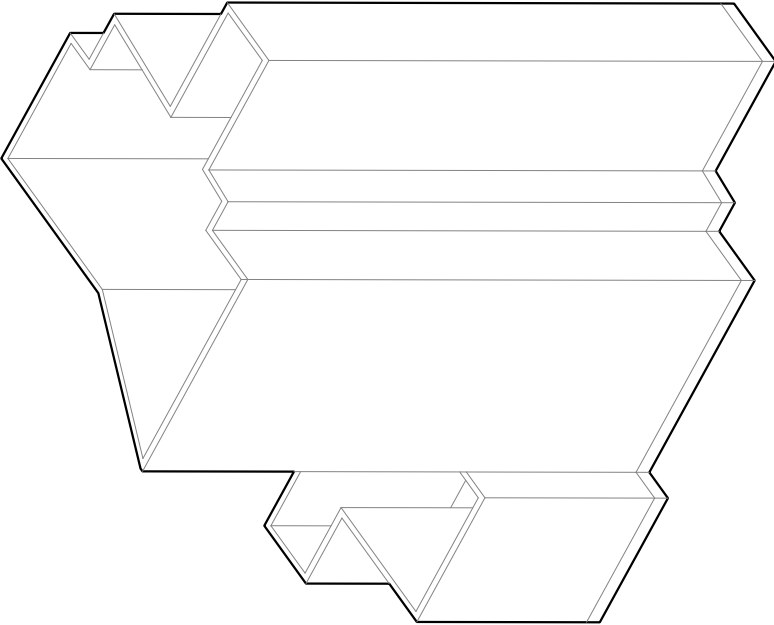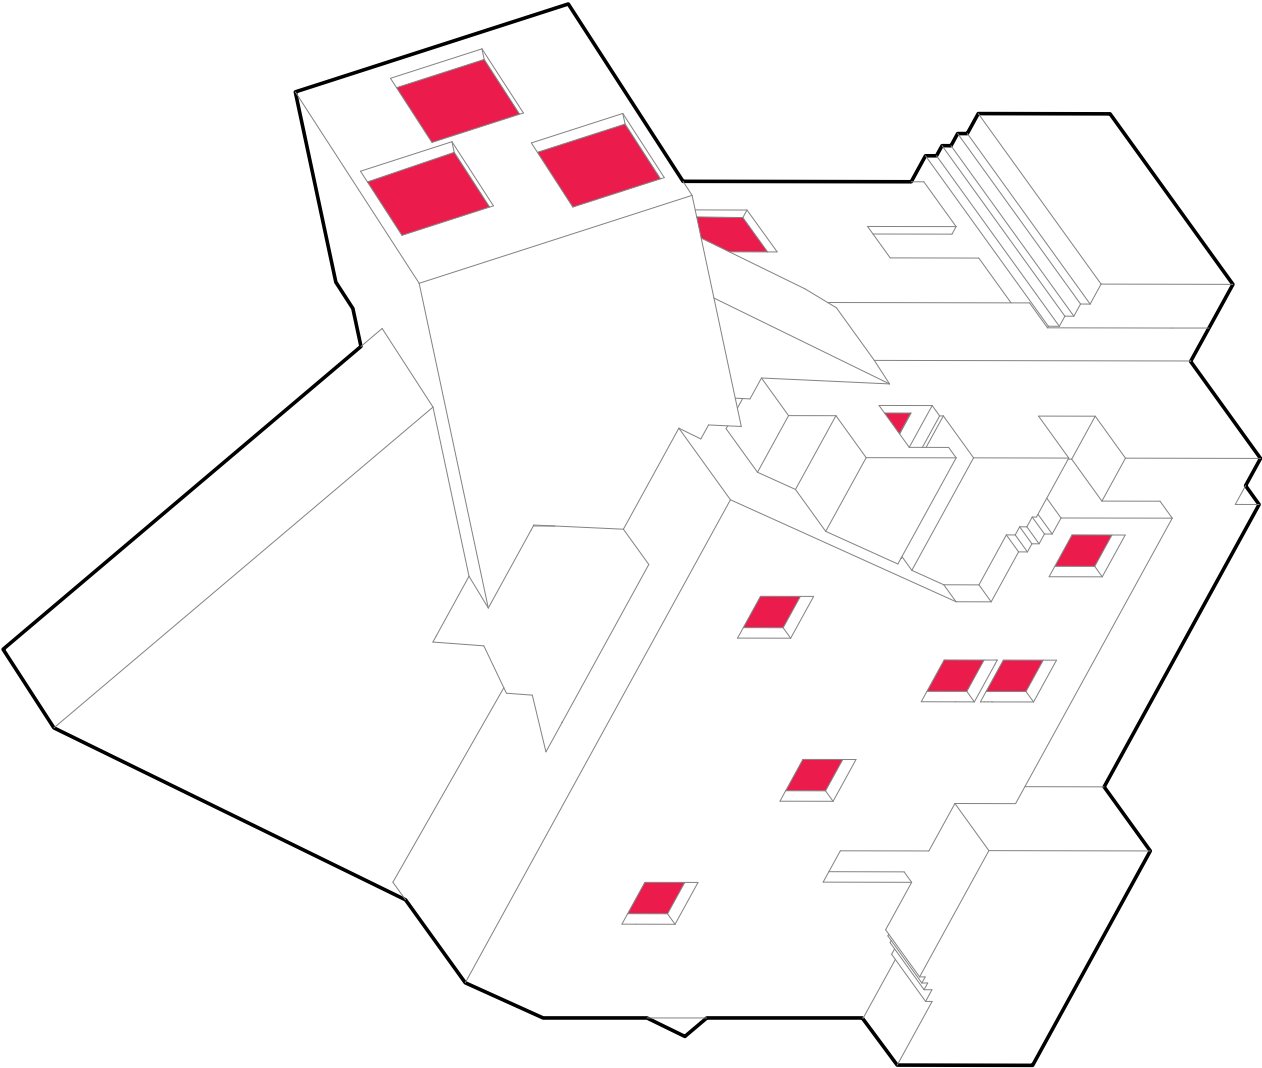

Triangle block toy
ALTANKHUYAGdash

